



Meyer/Shaffer Property
2224 Main Street
Garage Plan



Jeffrey M. Kalban and Associates Architecture, Inc.

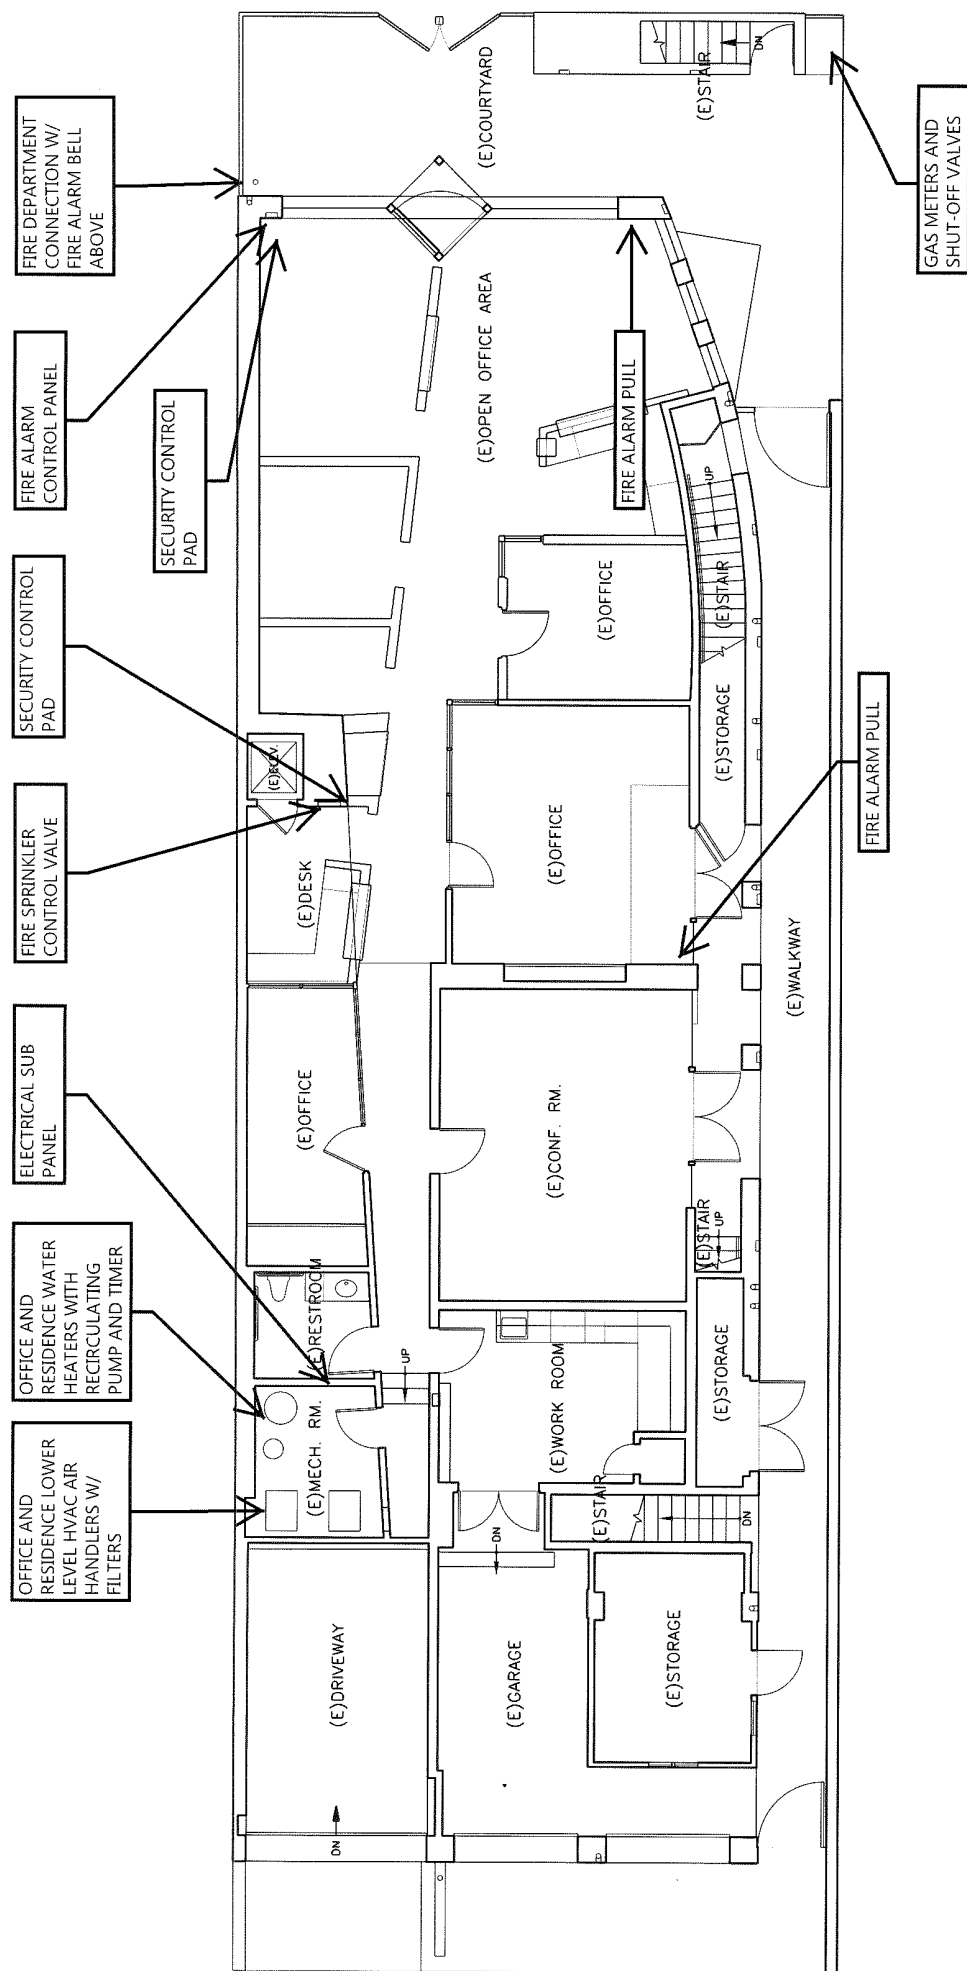

Meyer/Shaffer Property
2224 Main Street
Ground Floor Plan


Jeffrey M. Kalban and Associates Architecture, Inc.

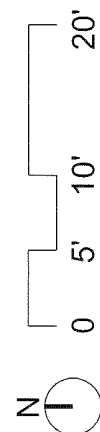

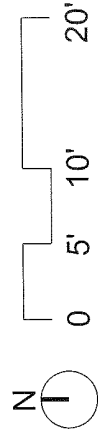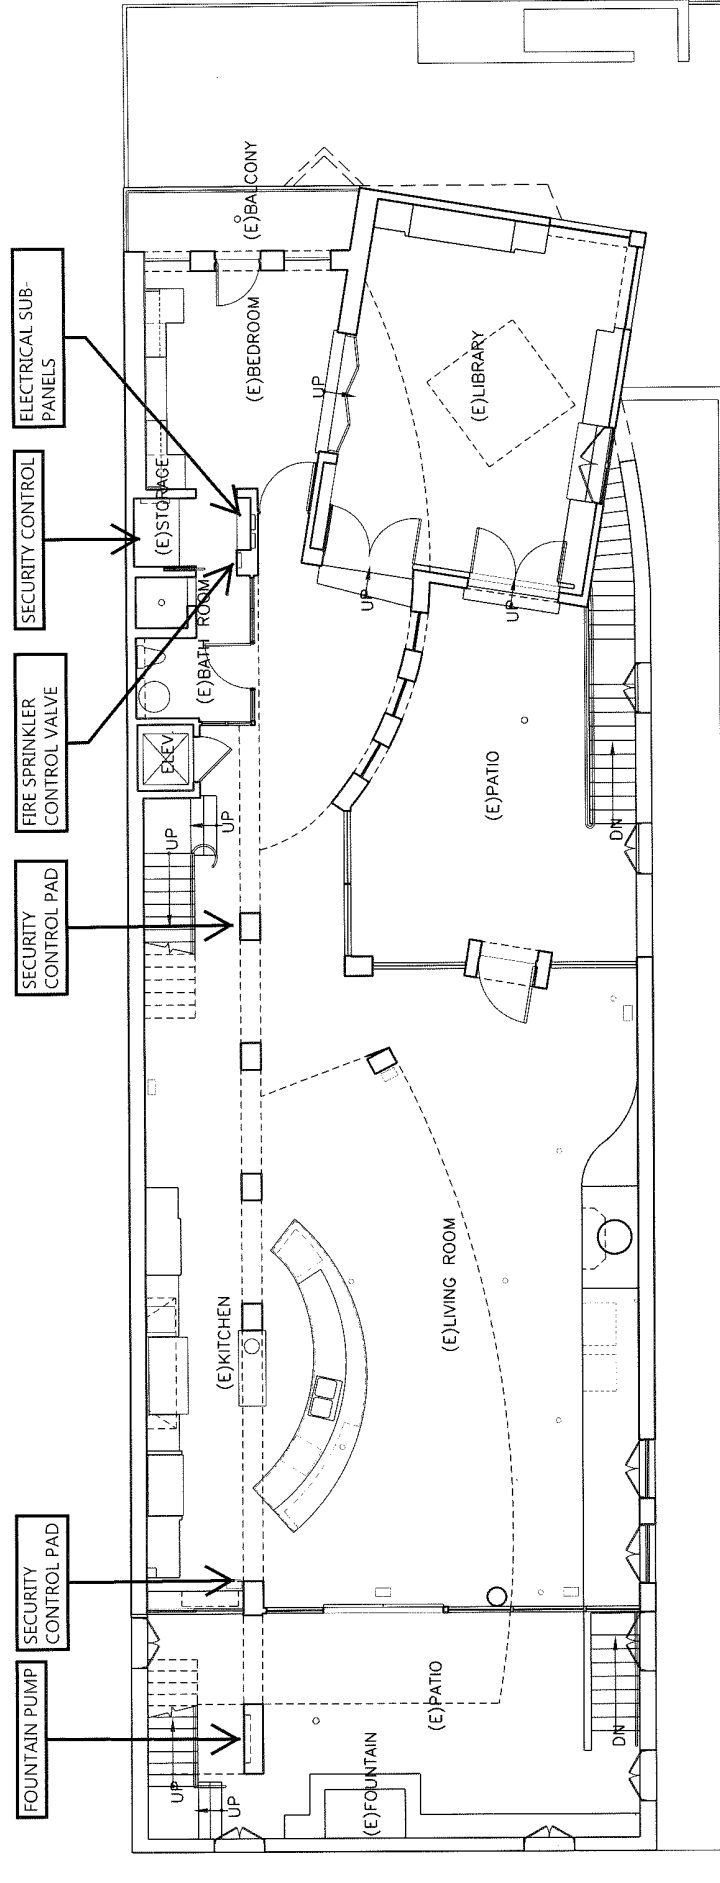


Meyer/Shaffer Property
2224 Main Street
Second Floor Plan


Jeffrey M. Kalban and Associates Architecture, Inc.

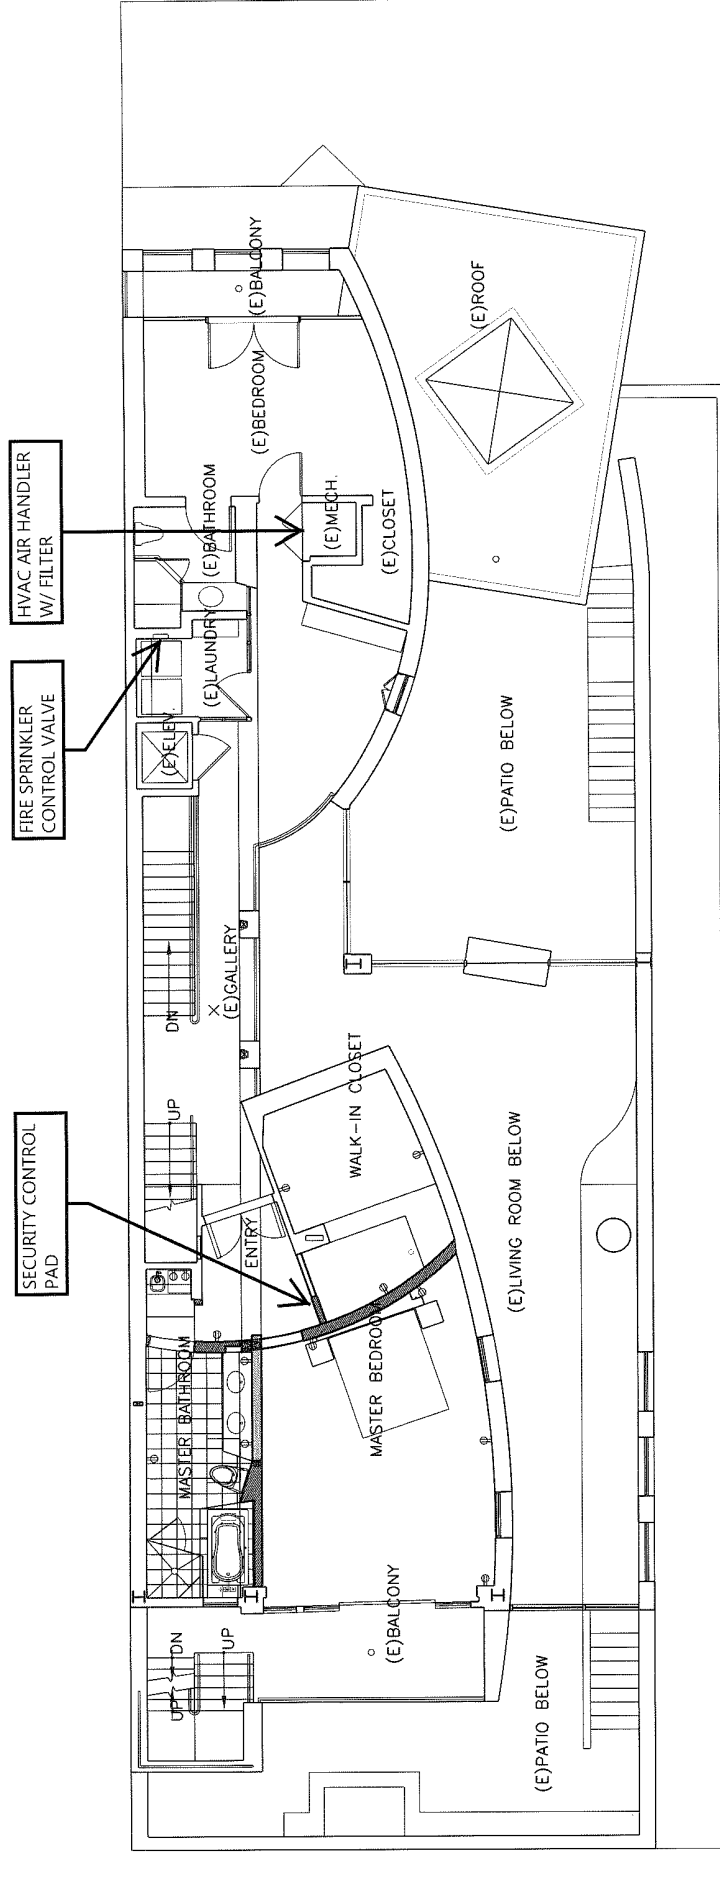


Meyer/Shaffer Property
2224 Main Street
Third Floor Plan

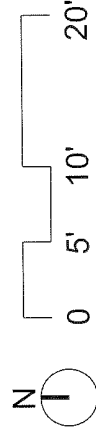


Jeffrey M. Kalban and Associates Architecture, Inc.

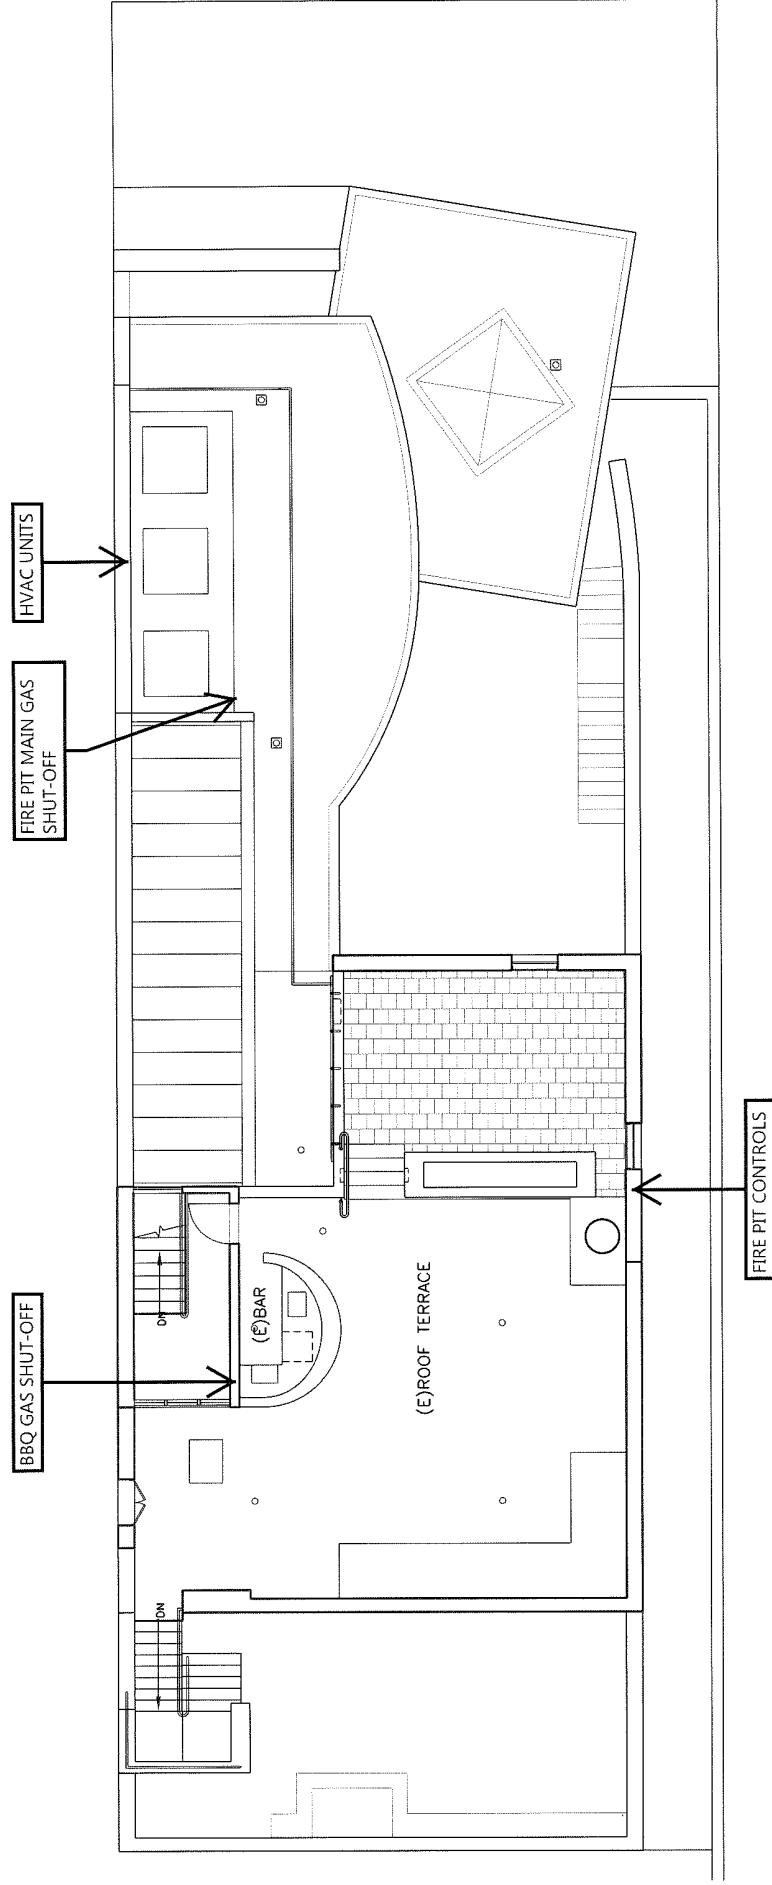


Meyer/Shaffer Property
2224 Main Street
Roof Terrace Plan

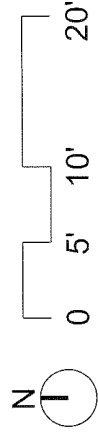


Jeffrey M. Kalban and Associates Architecture, Inc.

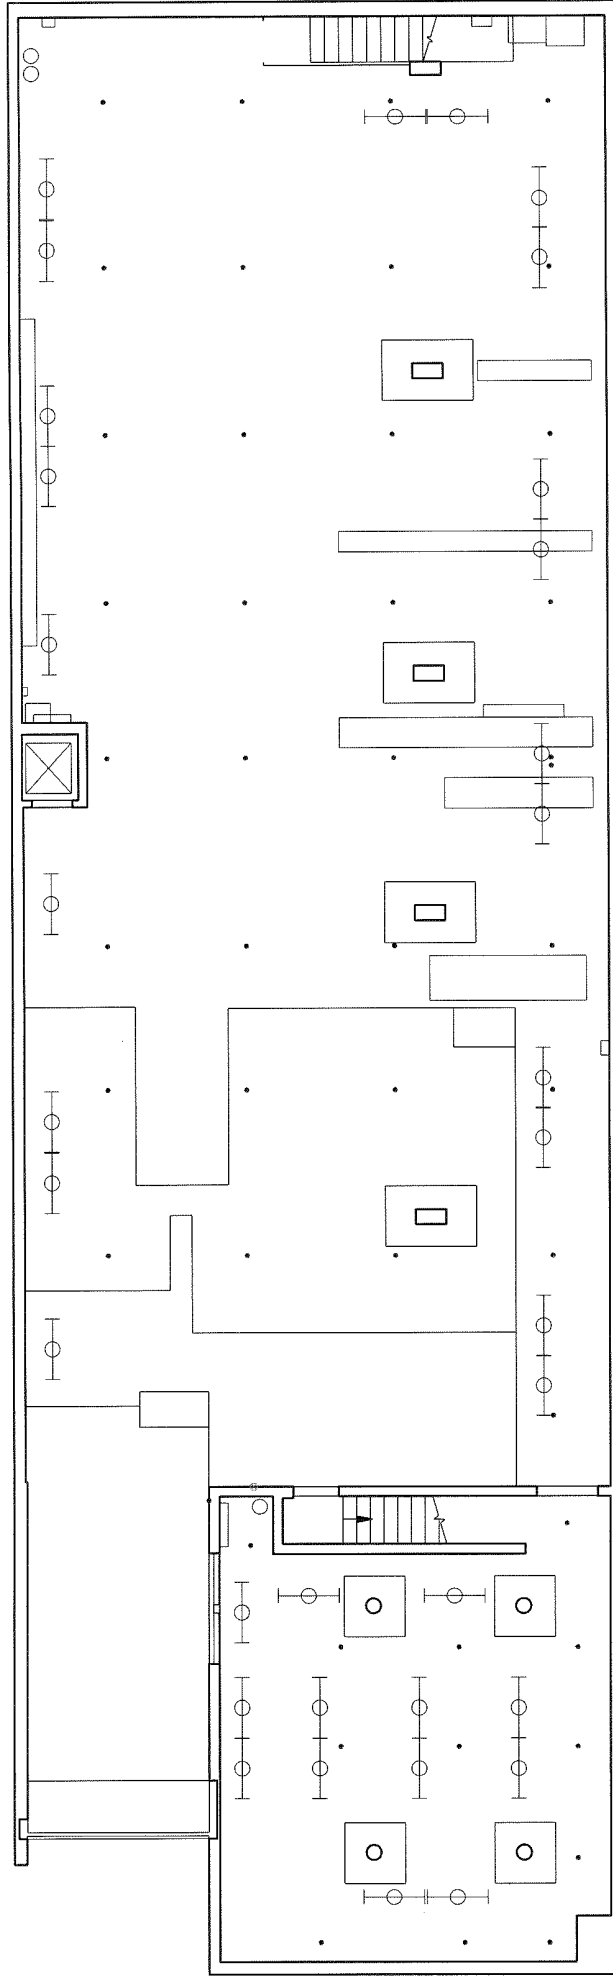

Meyer/Shaffer Property
 2224 Main Street
 Garage Ceiling Plan

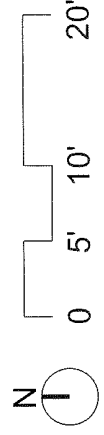


Jeffrey M. Kalban and Associates Architecture, Inc.

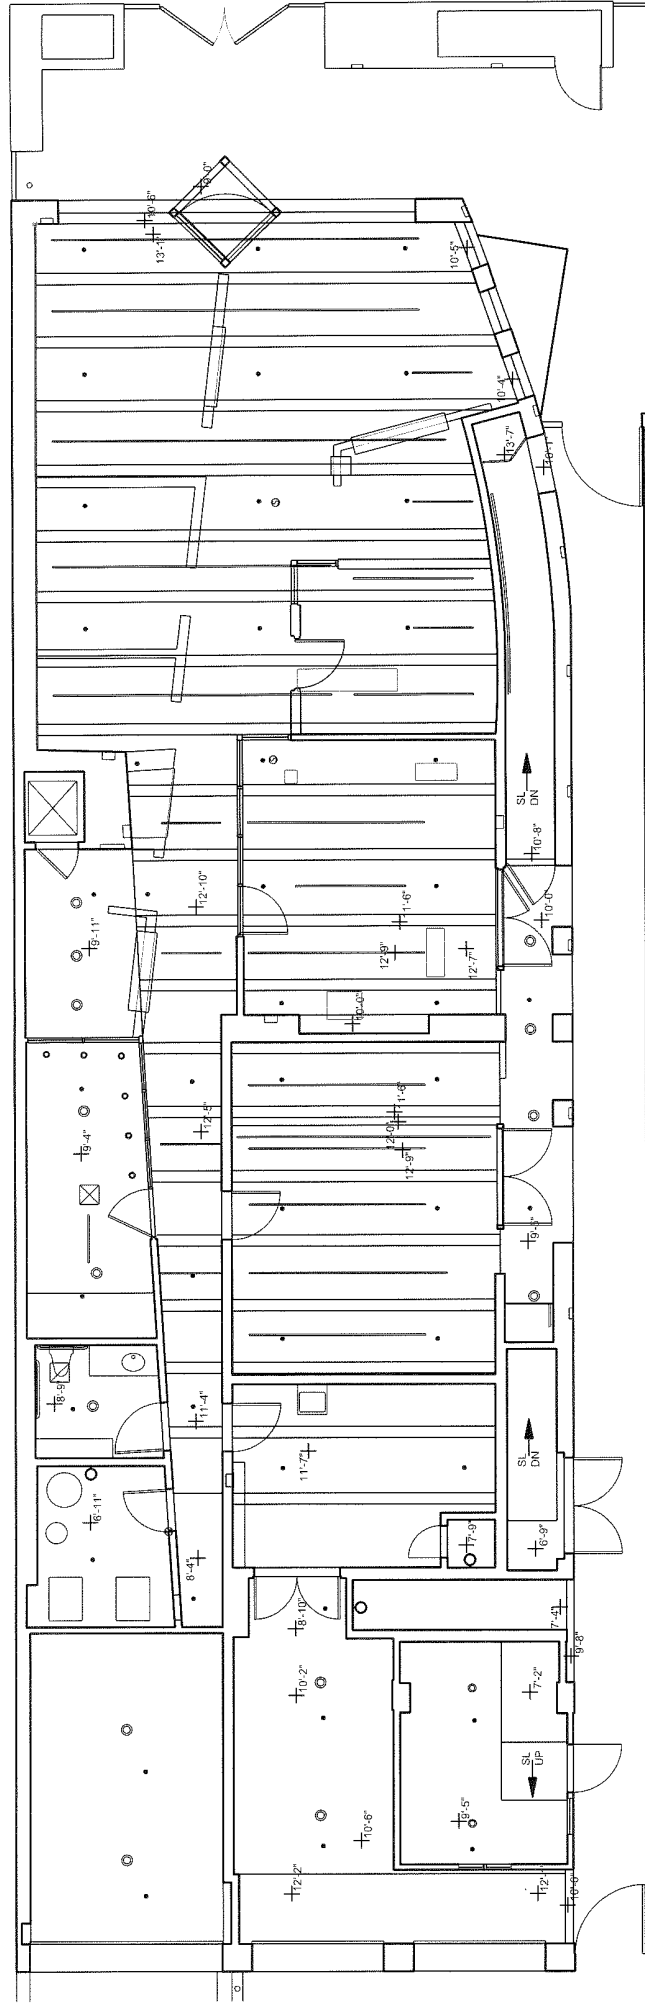


Meyer/Shaffer Property
2224 Main Street
Ground Floor Ceiling Plan



Jeffrey M. Kalban and Associates Architecture, Inc.

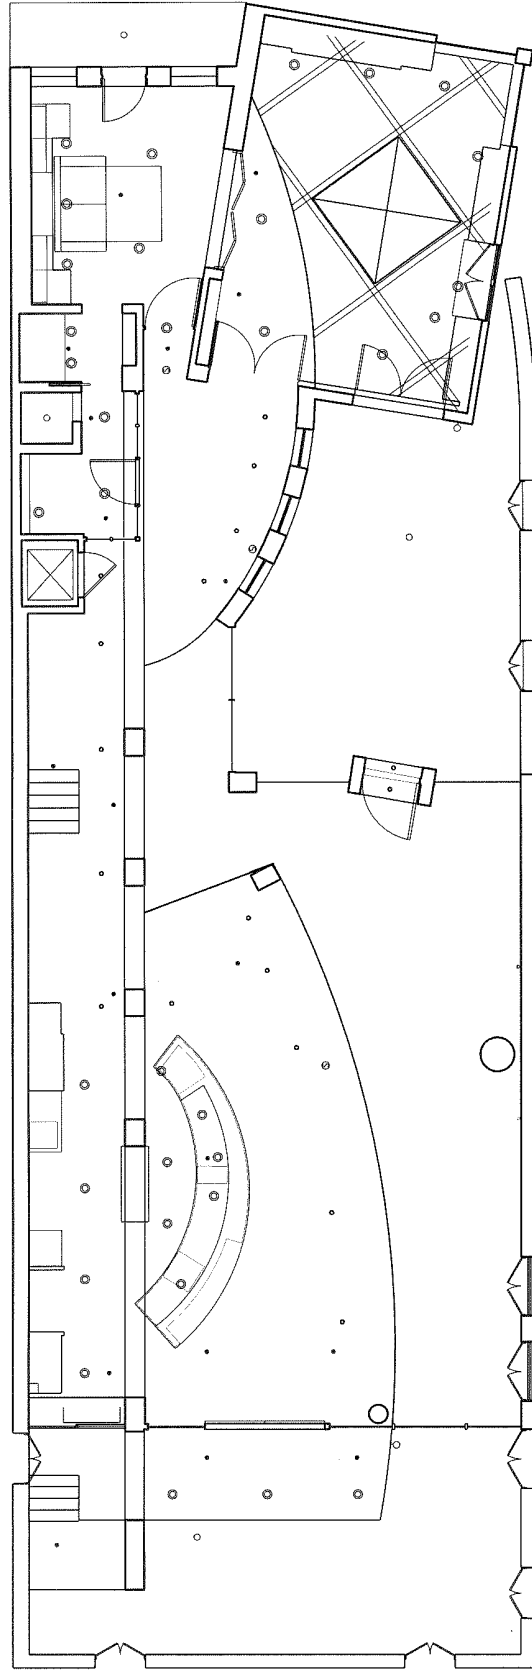

Meyer/Shaffer Property
2224 Main Street
Second Floor Ceiling Plan

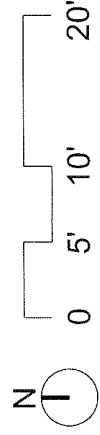

Jeffrey M. Kalban and Associates Architecture, Inc.

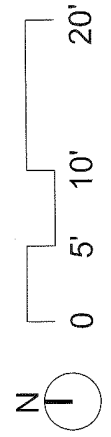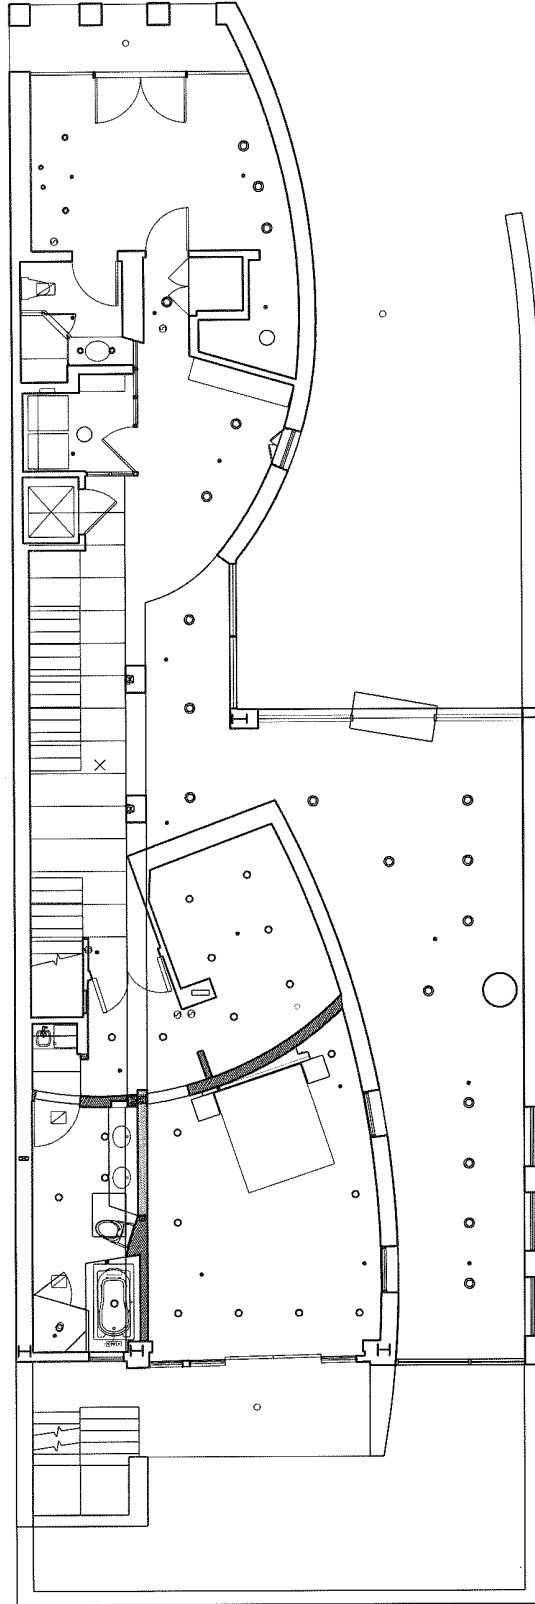

Meyer/Shaffer Property
2224 Main Street
Third Floor Ceiling Plan

Jeffrey M. Kalban and Associates Architecture, Inc.